

CUADRO DE PIEZAS

CÓDIGO	PIEZA	MEDIDA	CANT
MG120	Divisor orinal 12mm	60 × 120	2
PLCEN	Pilastra 12mm	16 × 180	3
PLLAT	Pilastra 12mm	16 × 180	1
PLLATMUR	Pilastra 12mm	16 × 180	1
PNCEN	Panel 12mm	150 × 150	3
PNLAT	Panel 12mm	150 × 150	1
PTADER	Puerta 12mm	95 × 150	4

TOTAL DE PIEZAS 15

HERRAJES

Juego completo en negro


420 cm

105

105

105

105

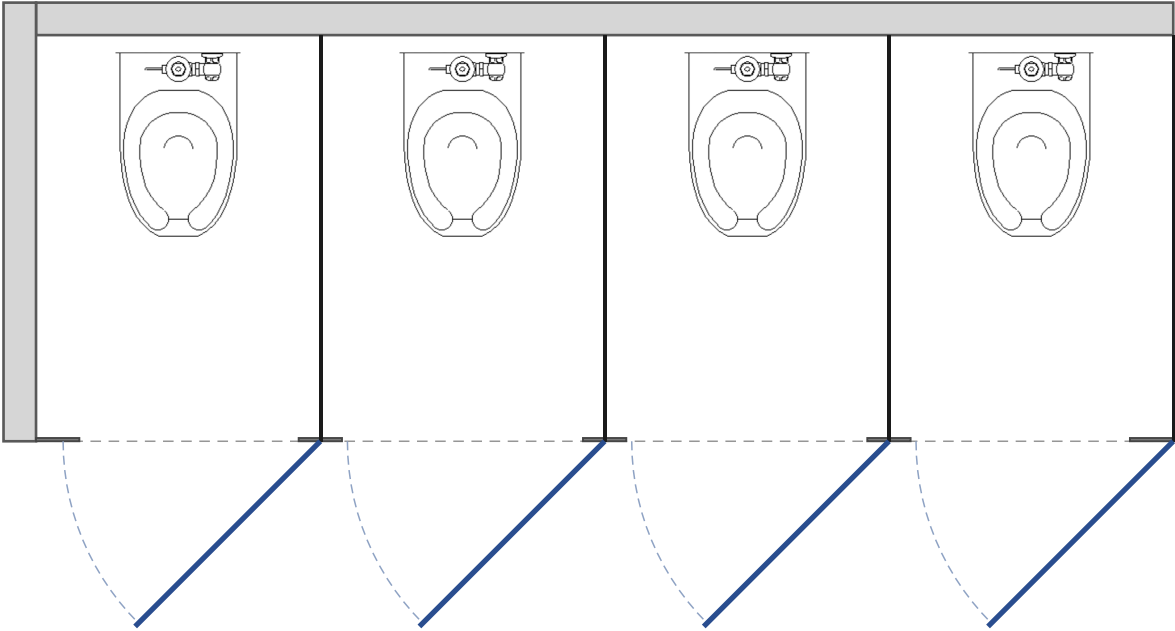

ESCALA 1:28

OBRA
Torre Escazú

CLIENTE
Constructora Volio

UBICACIÓN
San José, Escazú

ÁREA
Baño de hombres 101

PISO
Planta baja

TIPOLOGÍA
Recta con muro izquierdo

LÍNEA / MODELO
LEEDER · Estándar

ACABADO / COLOR
Laminado Compacto · BLANCO


ESPESOR · ALTO · PROF · SISTEMA
12 mm · 150 · 150 · Zoclo

N° DE PLANO
1042

DIBUJÓ
Dayanna Lizano

FECHA / HOJA
15/8/2026 · 1 de 4

GRUPO MODUMEX

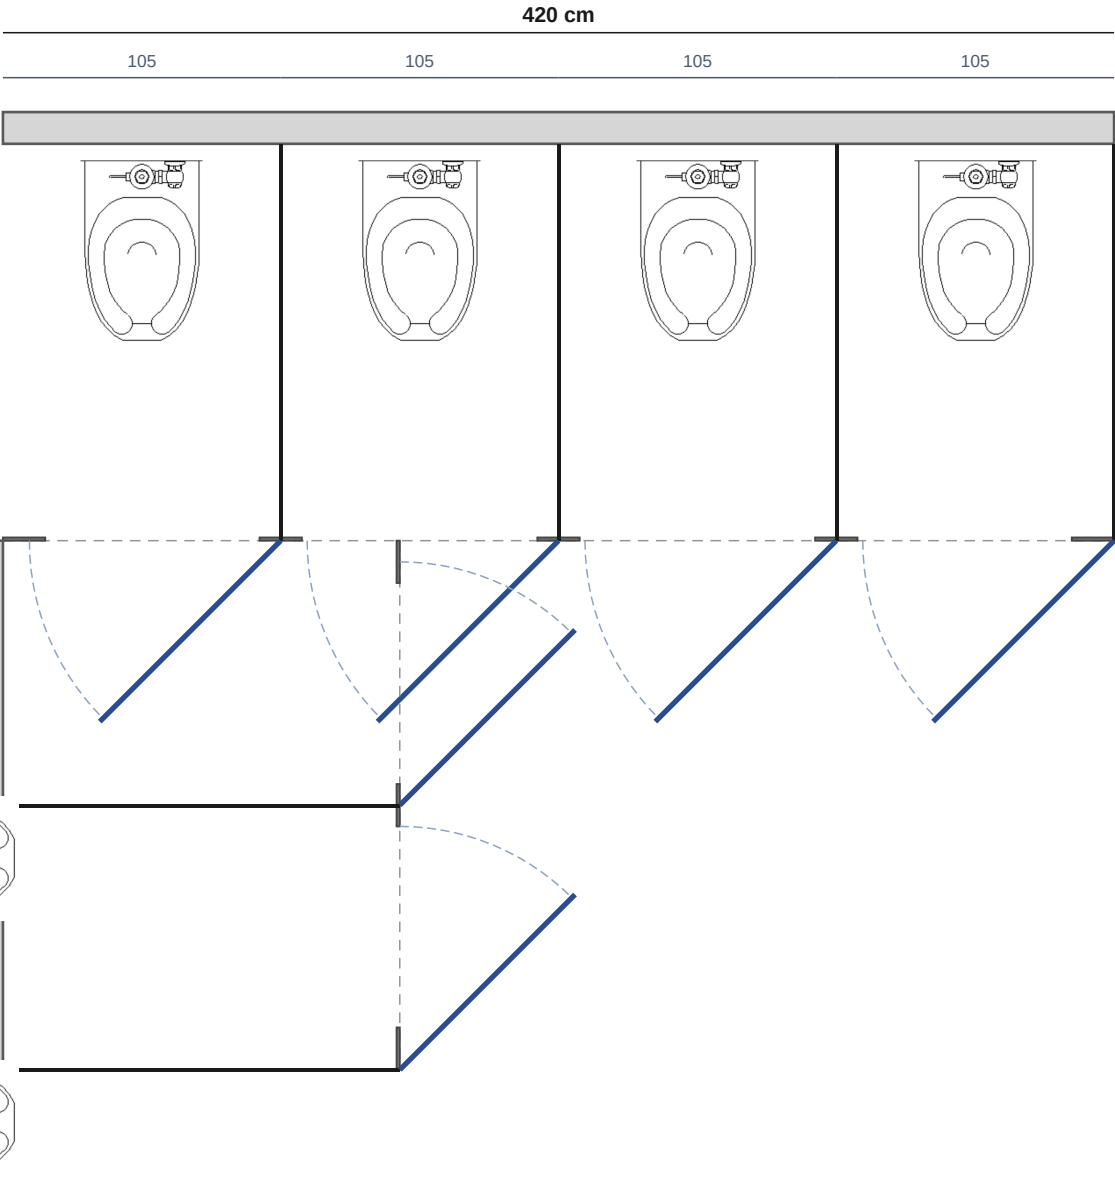

CUADRO DE PIEZAS

CÓDIGO	PIEZA	MEDIDA	CANT
MG120	Divisor orinal 12mm	60 × 120	2
PLCEN	Pilastra 12mm	16 × 180	4
PLLAT	Pilastra 12mm	16 × 180	2
PLLATMUR	Pilastra 12mm	16 × 180	1
PNCEN	Panel 12mm	150 × 150	4
PNLAT	Panel 12mm	150 × 150	2
PTADER	Puerta 12mm	95 × 150	4
PTADER	Puerta 12mm	92 × 150	2

TOTAL DE PIEZAS 21

HERRAJES

Juego completo en negro

ESCALA 1:29

OBRA
Torre Escazú

CLIENTE
Constructora Volio

UBICACIÓN
San José, Escazú

ÁREA
Baño de mujeres 102

PISO
Planta baja

TIPOLOGÍA
Esquina izquierda

LÍNEA / MODELO
LEEDER · Estándar

ACABADO / COLOR
Laminado Compacto · BLANCO


ESPESOR · ALTO · PROF · SISTEMA
12 mm · 150 · 150 · Zoclo

N° DE PLANO
1042

DIBUJÓ
Dayanna Lizano

FECHA / HOJA
15/8/2026 · 2 de 4

GRUPO MODUMEX

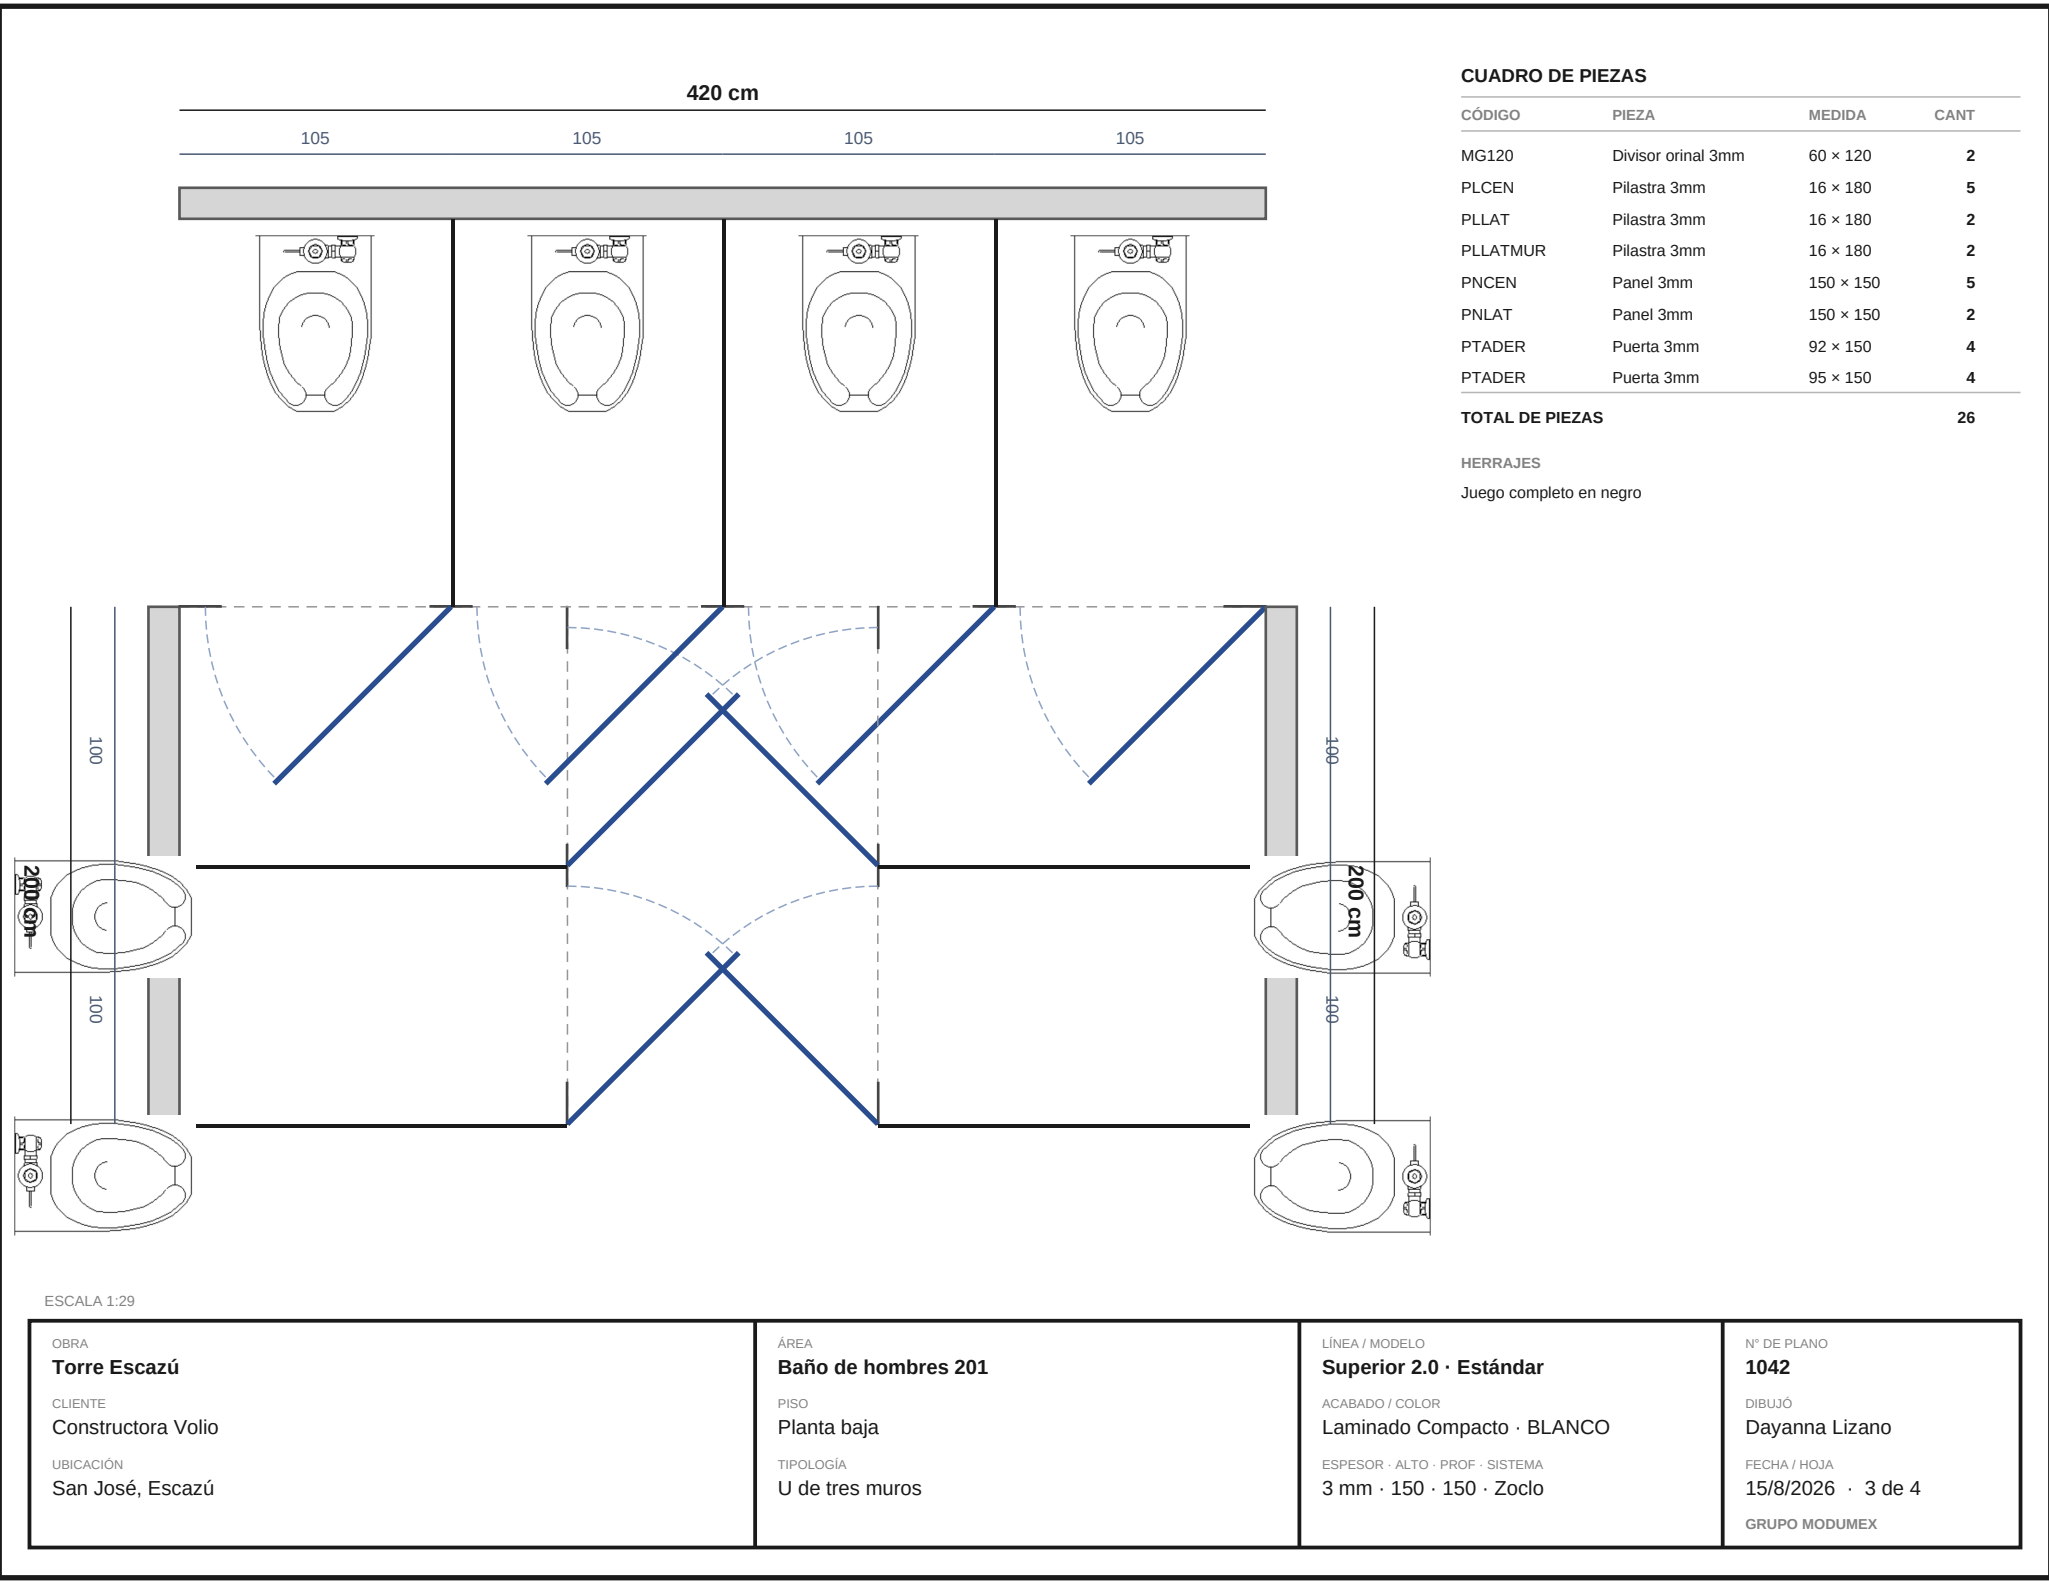

CUADRO DE PIEZAS

CÓDIGO	PIEZA	MEDIDA	CANT
MG120	Divisor orinal 3mm	60 × 120	2
PLCEN	Pilastra 3mm	16 × 180	5
PLLAT	Pilastra 3mm	16 × 180	2
PLLATMUR	Pilastra 3mm	16 × 180	2
PNCEN	Panel 3mm	150 × 150	5
PNLAT	Panel 3mm	150 × 150	2
PTADER	Puerta 3mm	92 × 150	4
PTADER	Puerta 3mm	95 × 150	4

TOTAL DE PIEZAS 26

HERRAJES

Juego completo en negro

ESCALA 1:29

OBRA
Torre Escazú

CLIENTE
Constructora Volio

UBICACIÓN
San José, Escazú

ÁREA
Baño de hombres 201

PISO
Planta baja

TIPOLOGÍA
U de tres muros

LÍNEA / MODELO
Superior 2.0 · Estándar

ACABADO / COLOR
Laminado Compacto · BLANCO

ESPESOR · ALTO · PROF · SISTEMA
3 mm · 150 · 150 · Zoclo

N° DE PLANO
1042

DIBUJÓ
Dayanna Lizano

FECHA / HOJA
15/8/2026 · 3 de 4

GRUPO MODUMEX


CUADRO DE PIEZAS

CÓDIGO	PIEZA	MEDIDA	CANT
MG120	Divisor orinal 12mm	60 × 120	4
PLCEN	Pilastra 12mm	16 × 180	3
PLLAT	Pilastra 12mm	16 × 180	1
PLLATMUR	Pilastra 12mm	16 × 180	1

TOTAL DE PIEZAS 9

HERRAJES

Juego completo en negro

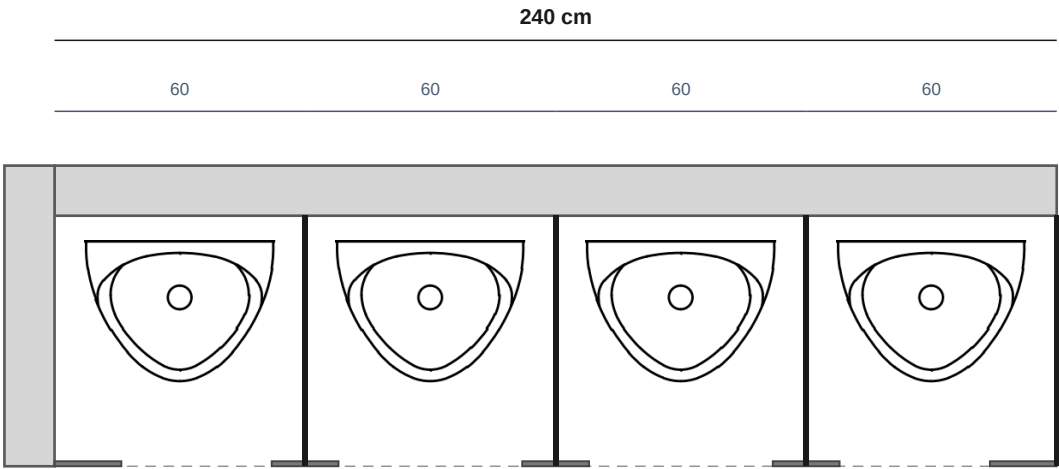

ESCALA 1:18

OBRA
Torre Escazú

CLIENTE
Constructora Volio

UBICACIÓN
San José, Escazú

ÁREA
Orinales 101

PISO
Planta baja

TIPOLOGÍA
Solo orinales

LÍNEA / MODELO
LEEDER · Estándar

ACABADO / COLOR
Laminado Compacto · BLANCO

ESPESOR · ALTO · PROF · SISTEMA
12 mm · 120 · 60 · Zoclo

N° DE PLANO
1042

DIBUJÓ
Dayanna Lizano

FECHA / HOJA
15/8/2026 · 4 de 4

GRUPO MODUMEX