

CUADRO DE PIEZAS

CÓDIGO	PIEZA	MEDIDA	CANT
MG120	Divisor orinal 12mm	60 × 120	2
PLCEN	Pilastra 12mm	55 × 180	3
PLLAT	Pilastra 12mm	10 × 180	1
PLLATMUR	Pilastra 12mm	10 × 180	1
PNCEN	Panel 12mm	150 × 150	3
PNLAT	Panel 12mm	150 × 150	1
PTADER	Puerta 12mm	60 × 150	4

TOTAL DE PIEZAS 15

HERRAJES

Juego completo en negro


425 cm

97.5

115

115

97.5

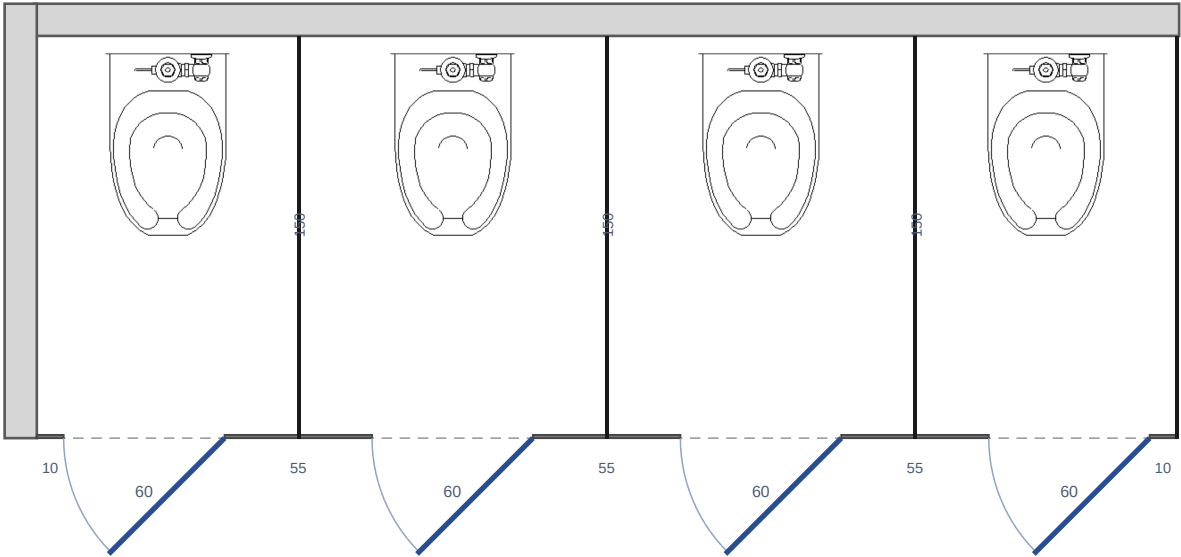

ESCALA 1:28

OBRA
Torre Escazú

CLIENTE
Constructora Volio

UBICACIÓN
San José, Escazú

ÁREA
Baño de hombres 101

PISO
Planta baja

TIPOLOGÍA
Recta con muro izquierdo

LÍNEA / MODELO
LEEDER · Estándar

ACABADO / COLOR
Laminado Compacto · BLANCO


ESPESOR · ALTO · PROF · SISTEMA
12 mm · 150 · 150 · Zoclo

N° DE PLANO
1042

DIBUJÓ
Dayanna Lizano

FECHA / HOJA
15/8/2026 · 1 de 4

GRUPO MODUMEX

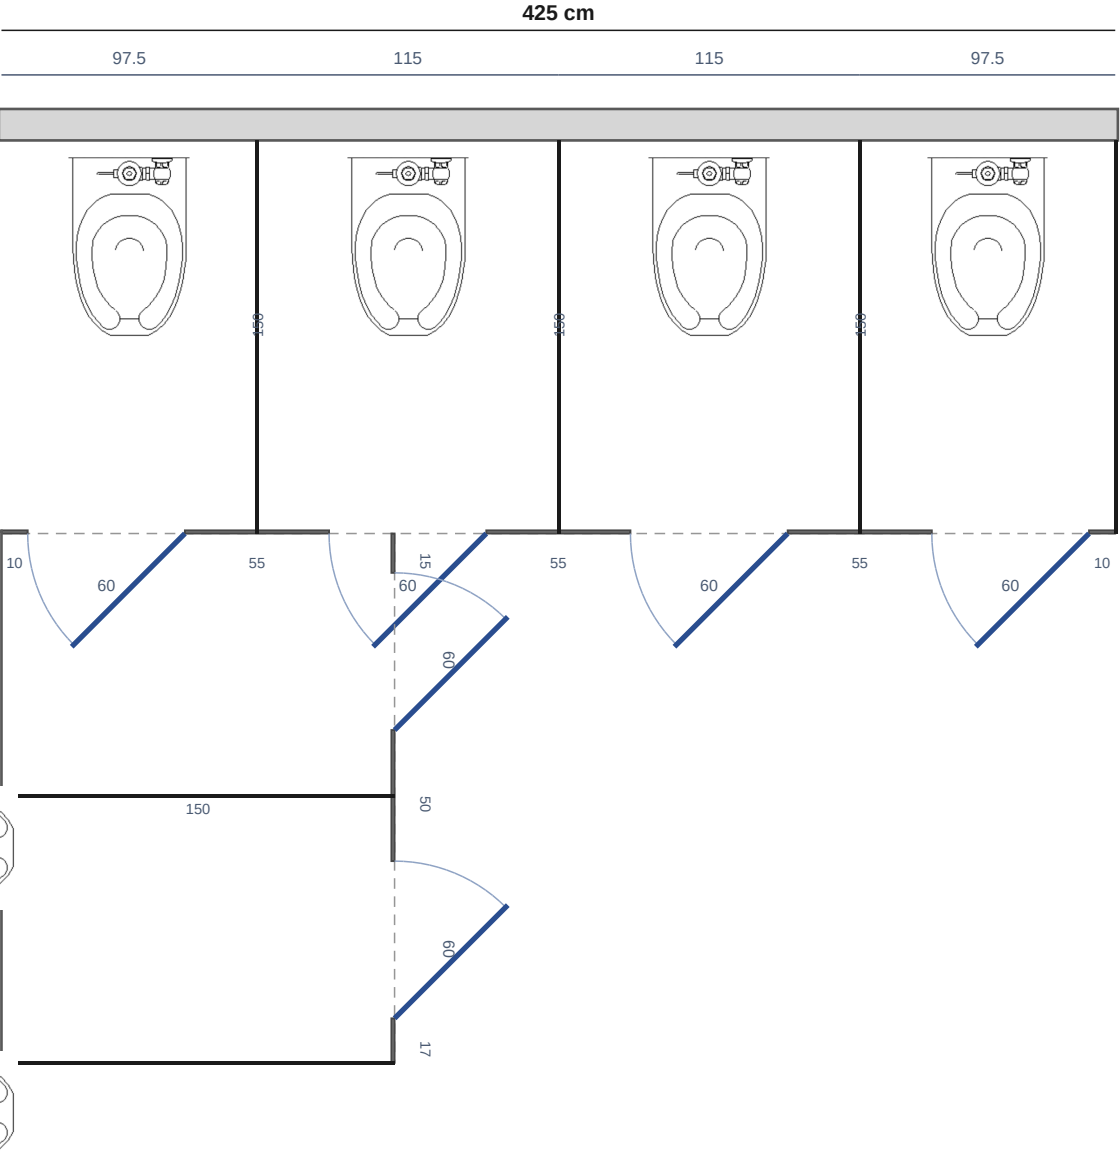

CUADRO DE PIEZAS

CÓDIGO	PIEZA	MEDIDA	CANT
MG120	Divisor orinal 12mm	60 × 120	2
PLCEN	Pilastra 12mm	55 × 180	3
PLCEN	Pilastra 12mm	50 × 180	1
PLLAT	Pilastra 12mm	10 × 180	1
PLLAT	Pilastra 12mm	17 × 180	1
PLLATMUR	Pilastra 12mm	10 × 180	1
PNCEN	Panel 12mm	150 × 150	4
PNLAT	Panel 12mm	150 × 150	2
PTADER	Puerta 12mm	60 × 150	6

TOTAL DE PIEZAS 21

HERRAJES

Juego completo en negro


ESCALA 1:29

OBRA
Torre Escazú
CLIENTE
Constructora Volio
UBICACIÓN
San José, Escazú

ÁREA
Baño de mujeres 102
PISO
Planta baja
TIPOLOGÍA
Esquina izquierda

LÍNEA / MODELO
LEEDER · Estándar
ACABADO / COLOR
Laminado Compacto · BLANCO
ESPESOR · ALTO · PROF · SISTEMA
12 mm · 150 · 150 · Zoclo

N° DE PLANO
1042
DIBUJÓ
Dayanna Lizano
FECHA / HOJA
15/8/2026 · 2 de 4
GRUPO MODUMEX

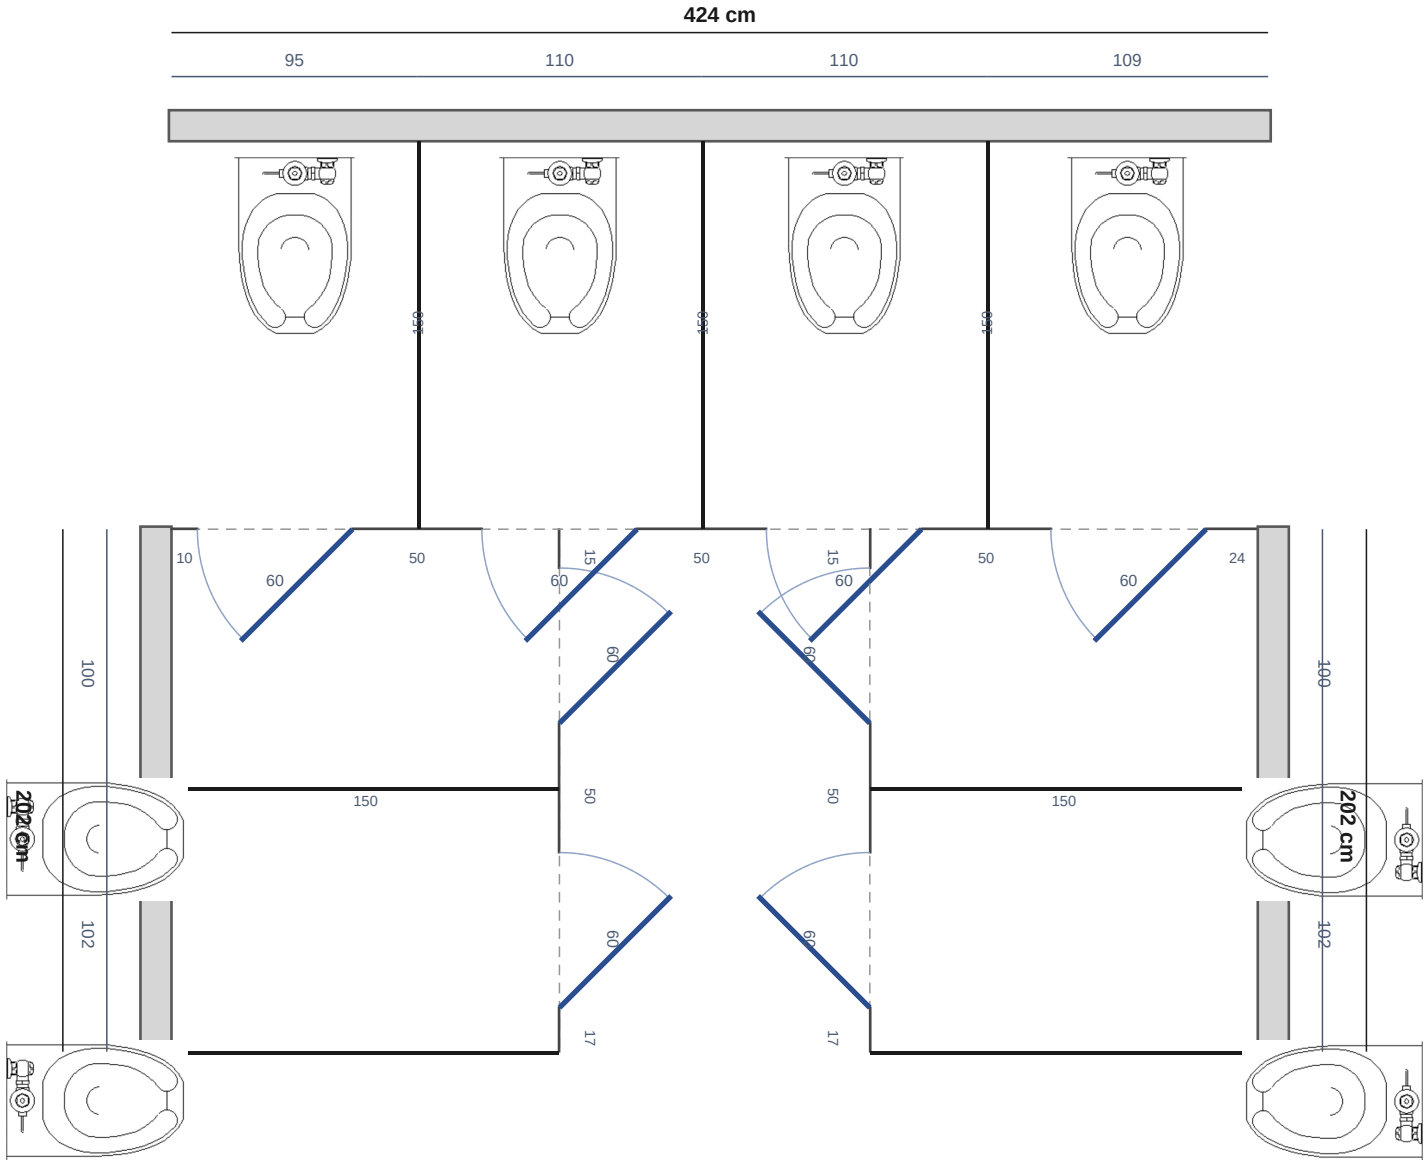

CUADRO DE PIEZAS

CÓDIGO	PIEZA	MEDIDA	CANT
MG120	Divisor orinal 3mm	60 × 120	2
PLCEN	Pilastra 3mm	50 × 180	5
PLLAT	Pilastra 3mm	17 × 180	2
PLLATMUR	Pilastra 3mm	10 × 180	1
PLLATMUR	Pilastra 3mm	24 × 180	1
PNCEN	Panel 3mm	150 × 150	5
PNLAT	Panel 3mm	150 × 150	2
PTADER	Puerta 3mm	60 × 150	8

TOTAL DE PIEZAS 26

HERRAJES

Juego completo en negro

ESCALA 1:29

OBRA
Torre Escazú
CLIENTE
Constructora Volio
UBICACIÓN
San José, Escazú

ÁREA
Baño de hombres 201
PISO
Planta baja
TIPOLOGÍA
U de tres muros

LÍNEA / MODELO
Superior 2.0 · Estándar
ACABADO / COLOR
Laminado Compacto · BLANCO
ESPESOR · ALTO · PROF · SISTEMA
3 mm · 150 · 150 · Zoclo

N° DE PLANO
1042
DIBUJÓ
Dayanna Lizano
FECHA / HOJA
15/8/2026 · 3 de 4
GRUPO MODUMEX


CUADRO DE PIEZAS

CÓDIGO	PIEZA	MEDIDA	CANT
MG120	Divisor orinal 12mm	60 × 120	4
PLLAT	Pilastra 12mm	15 × 180	1
PLLATMUR	Pilastra 12mm	15 × 180	1

TOTAL DE PIEZAS 6

HERRAJES

Juego completo en negro

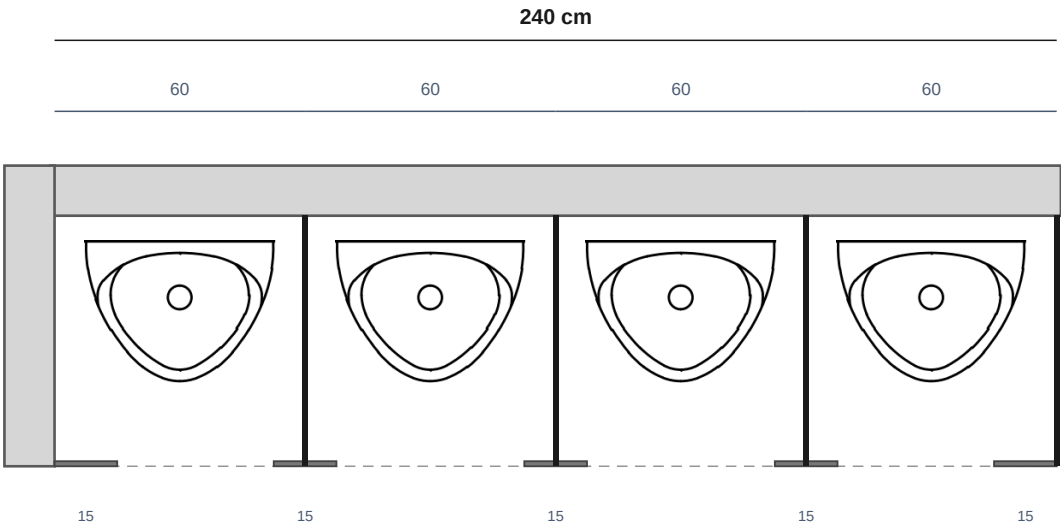

ESCALA 1:18

OBRA
Torre Escazú

CLIENTE
Constructora Volio

UBICACIÓN
San José, Escazú

ÁREA
Orinales 101

PISO
Planta baja

TIPOLOGÍA
Solo orinales

LÍNEA / MODELO
LEEDER · Estándar

ACABADO / COLOR
Laminado Compacto · BLANCO

ESPESOR · ALTO · PROF · SISTEMA
12 mm · 120 · 60 · Zoclo

N° DE PLANO
1042

DIBUJÓ
Dayanna Lizano

FECHA / HOJA
15/8/2026 · 4 de 4

GRUPO MODUMEX